PLANTA
(1:200)

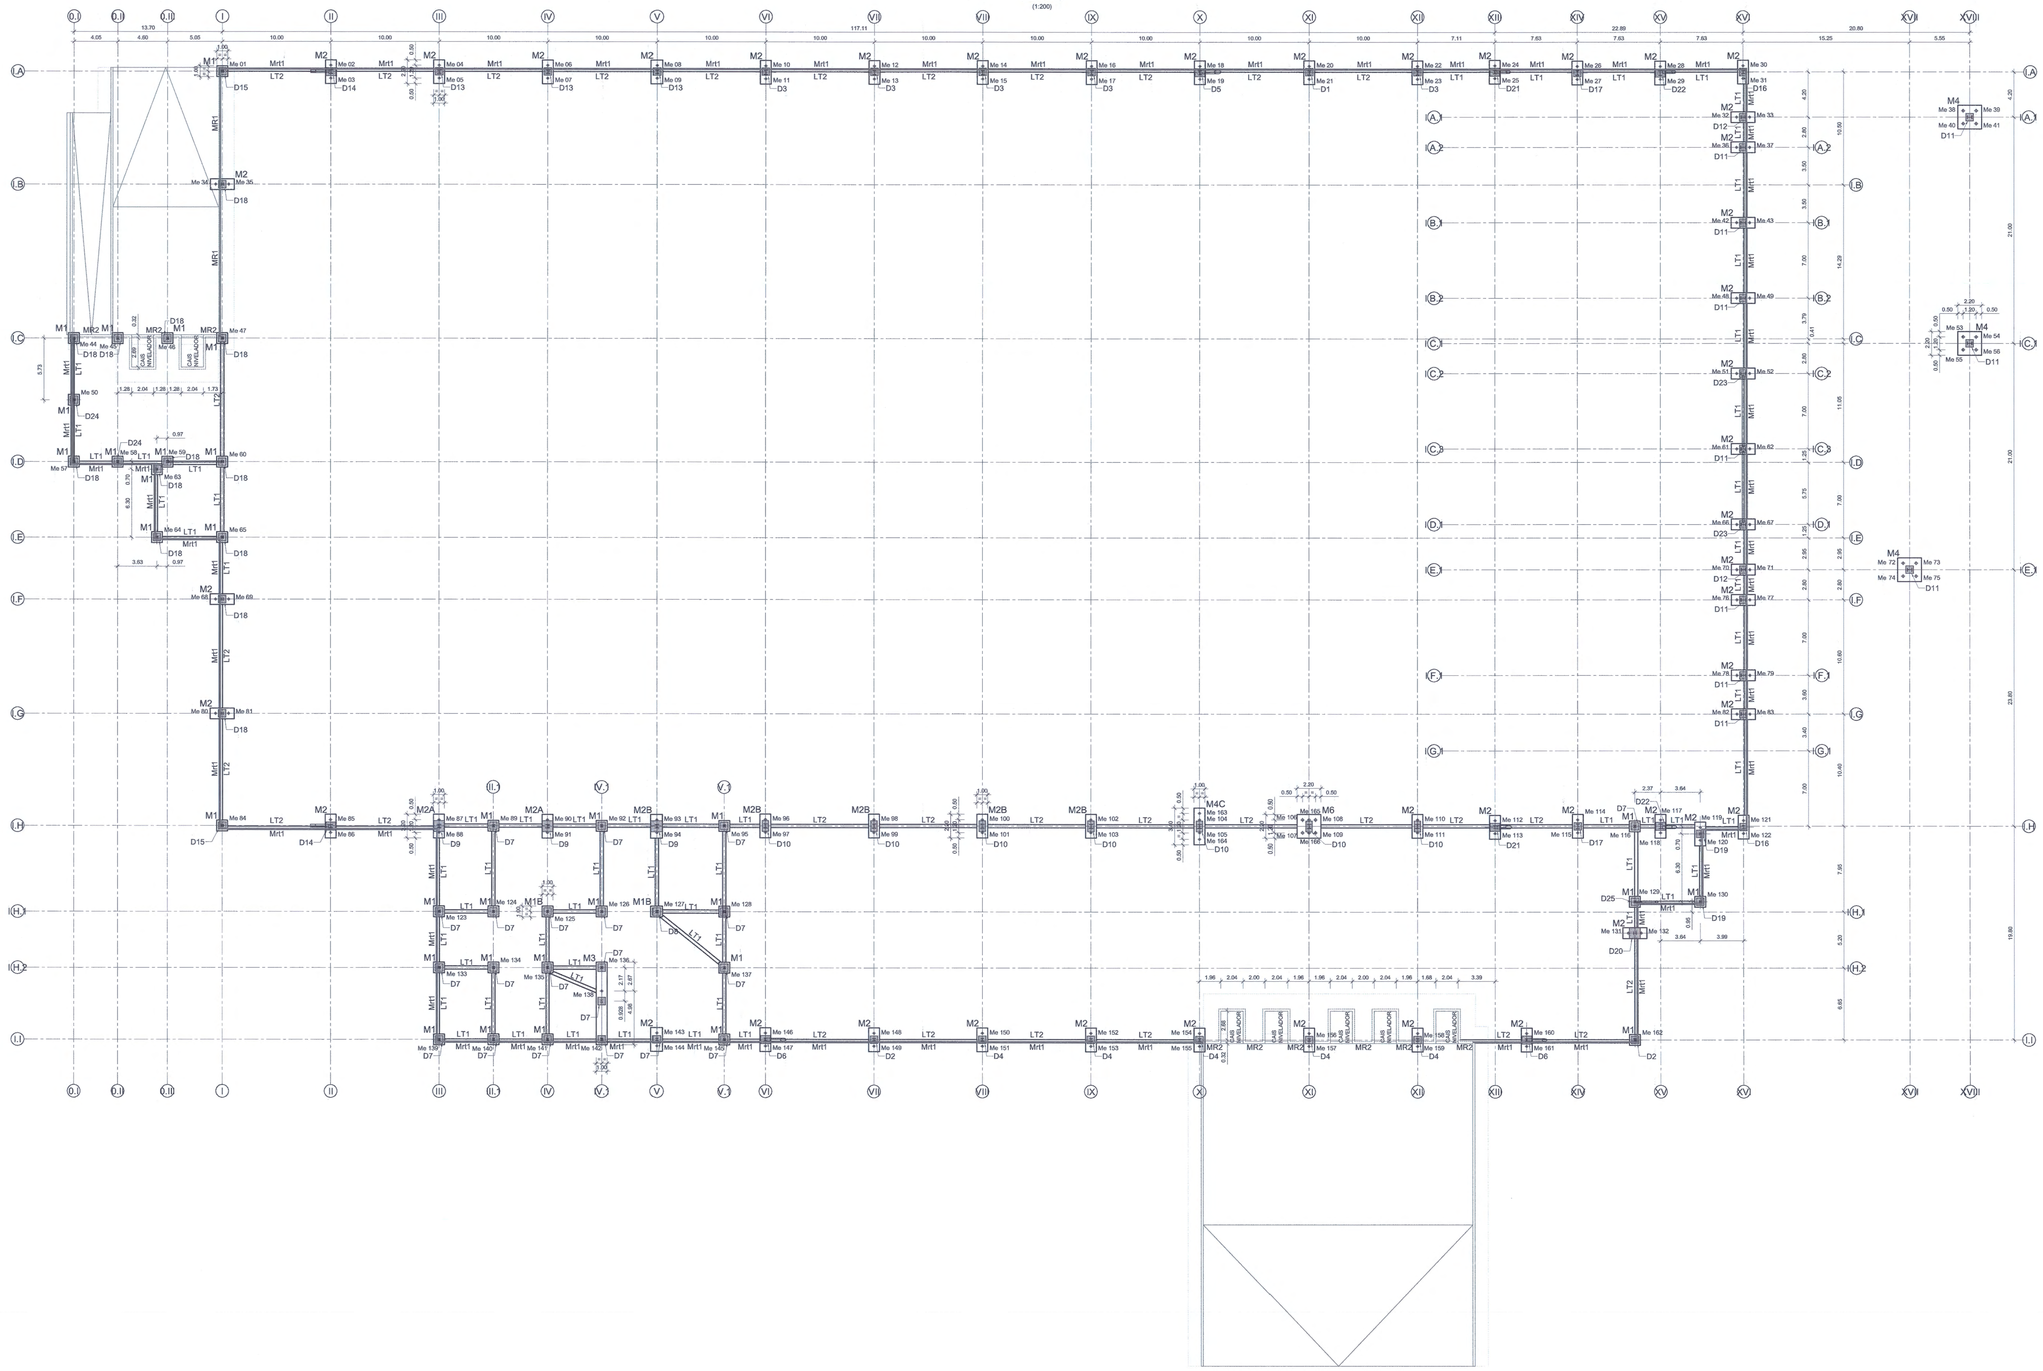

NOTAS

- IMPLANTAÇÃO DAS FUNDAÇÕES A CONFIRMAR E A REALIZAR PELO CLIENTE;
- IMPLANTAÇÃO ADOTADA PARA AS FUNDAÇÕES DESTE PROJETO TEM COMO BASE A PEÇA DESENHADA "435_PE_EST_01 - FASE I- PLANTA DO PISO 0" DATADA DE 31/03/2021 REFERENTE AO PROJETO DE ESTRUTURAS DA SE2P E DA METALOVIANA;
- AS FUNDAÇÕES FORAM DIMENSIONADAS DE ACORDO COM O PLANO DE CARGAS DISPONIBILIZADO PELO CLIENTE NA PEÇA DESENHADA "XRF.2020046-P.000.EST.SSE.MAPACARGASR02_SE2P";
- PLINTOS D1 a D25 A EXECUTAR CONFORME DIMENSÕES E ARMADURAS DEFINIDAS NO PROJETO DE ESTRUTURAS DA SE2P E DA METALOVIANA.

PLANTA DE LOCALIZAÇÃO
(S.E)

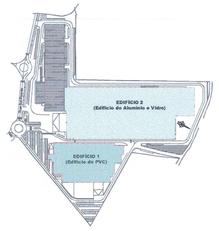

MURETE Mrt1
(1:50)

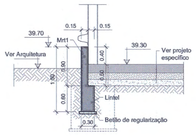

MURO MR1
(1:50)

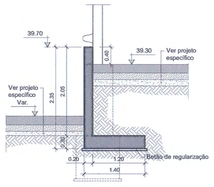

MURO MR2
(1:50)

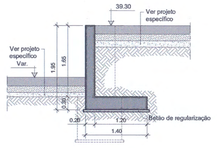

CAIS NIVELADORES
(1:50)

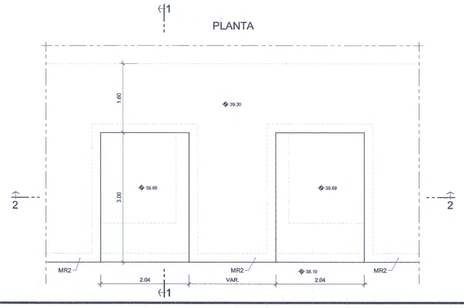

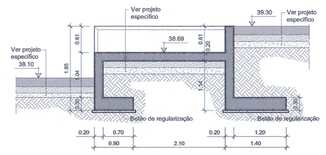

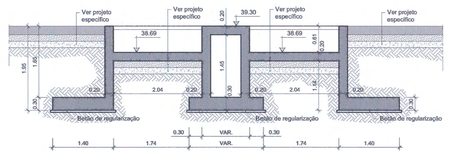

Revisão	Designação	Date	Desenhado	Projetado

TRYBA, SA
AMPLIAÇÃO DA FÁBRICA TRYBA CAIXIAVE

TEIXEIRA DUARTE
ENGENHARIA E CONSTRUÇÕES, S.A.

AMPLIAÇÃO DA FÁBRICA TRYBA CAIXIAVE

RUA SOL POENTE, Nº 125, RIBEIRÃO
VILA NOVA DE FAMALICÃO

PROJETO DE EXECUÇÃO
FUNDAÇÕES
EDIFÍCIO 1
DIMENSIONAMENTO

Projetado	Desenhado	Verificado	Aprovado

Projeto Nº	Nº Caldeação	Nº Registo	Revisão
P7358	PE-GE05-1-01-001	271436	-

Substitui desenho nº
-
Anexo à nossa Proposta Ref.ª
-

PLANTAS E CORTES

Data	Escala	Nome do fichei
2021-04-16	1:200 1:50	P7358 PE-GE05-1-01-001 271436.dwg

Este desenho é propriedade da Teixeira Duarte e não pode ser reproduzido sem autorização expressa | Todos os direitos reservados pela legislação em vi gor.

Formato A0
1.189x841mm